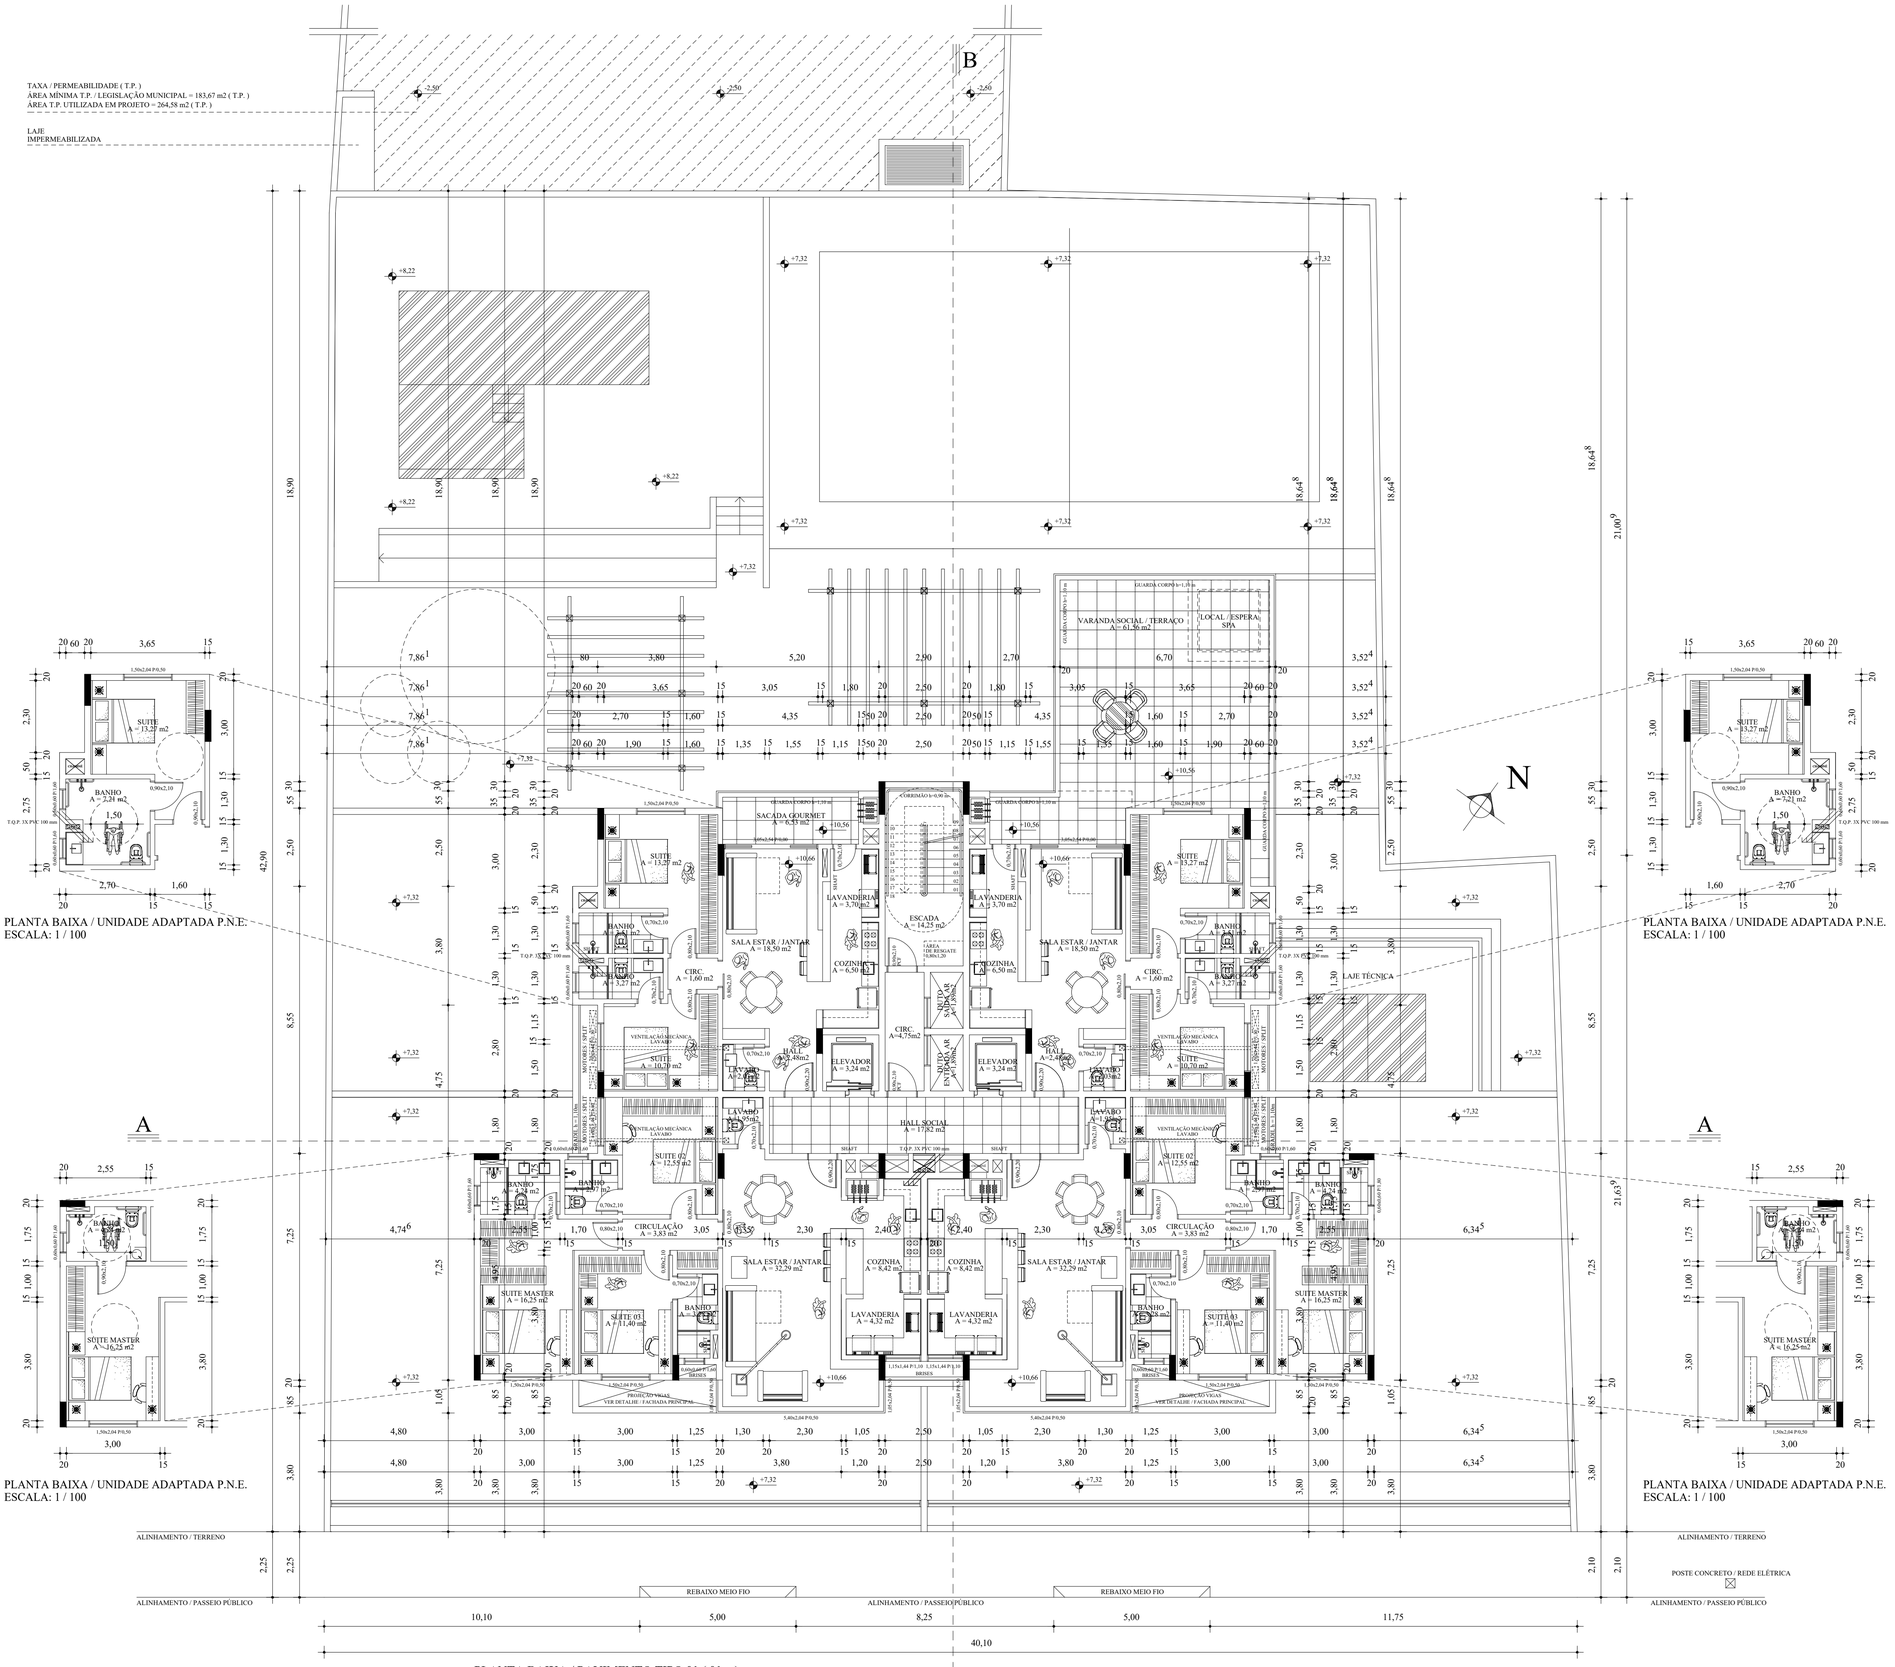

PLANTA BAIXA / UNIDADE ADAPTADA P.N.E.
ESCALA: 1 / 100

PLANTA BAIXA / UNIDADE ADAPTADA P.N.E.
ESCALA: 1 / 100

PLANTA BAIXA / UNIDADE ADAPTADA P.N.E.
ESCALA: 1 / 100

PLANTA BAIXA / UNIDADE ADAPTADA P.N.E.
ESCALA: 1 / 100

PLANTA BAIXA / PAVIMENTO TIPO 01 (01 x)
*** ÁREA / PAVIMENTO TIPO 01 = 522,20 m2
ÁREA TOTAL = 11.810,34 m2
ESCALA: 1 / 100 *** ÁREA / TERRENO = 1.836,78 m2

REVISÃO	DATA	DESCRIÇÃO	RESPONSÁVEL

CONSTRUTORA SENGER
CARAZINHO - Rua Barão de Antonina, 79 - sala 201
Fone / Fax: (54) 3331-2756 / 3331-2759
e-mail: sengerconstrutora@gmail.com
site: www.construtorasenger.com.br

OBRA:
EDIFÍCIO MULT. RESIDENCIAL / COMERCIAL

LOCAL:
RUA VENÂNCIO AIRES, LADO ÍMPAR / CENTRO - CARAZINHO RS

PROJETO: ARQUITETÔNICO | A | 06

PROJETO ARQUITETÔNICO:
Arq. Rafael Baú Branda CAU A33474-0

PROJETOS COMPLEMENTARES:

EXECUÇÃO:
Construtora Senger Ltda CREA 38180

PROPRIETÁRIO:
Construtora Senger Ltda

PRANCHA:
PLANTA BAIXA
PAVIMENTO TIPO 01
PAVIMENTO 05

ESCALA:	ÁREA TOTAL:	DATA:
1 : 100	A=11.810,34m2	MAR. / 2026